

2nd Floor

STERILE PROCESSING

**OPEN TO
LOBBY
BELOW**

SURGERY WAITING

CATH

ENDC

PRE / POST

FUTURE AREAS
SHOWN IN BLUE

FUTURE PACU

STAFF ENTRY POINT

G-402

TRUE NORTH

3rd Floor

MED / SURG

ADMIN

PHYSICAL THERAPY

DIALYSIS

ICU

Current office standard sizes that HOR has:

JOB CLASSIFICATION	NET AREA SF (Range)	COMMENTS
SF/Hospital	225 / 140	Enclosed Office
VP Office	380 / 140	Enclosed Office
AVP / Senior Director Office	120 / 100	Enclosed Office
Director / Manager Office Type 1 (w/direct reports)	120 / 140	Enclosed Office / Open Workstation
Director / Manager Office Type 2 (w/direct reports)	100 / 140	Enclosed Office / Open Workstation
Workstation Type 1	48 / 36	Open Workstation
Workstation Type 2	36 / 30	Open Workstation

- Depending on the constraints of the space, standards may flex down to accommodate the program, but shall never exceed the maximum.
- Maximum workstation size in an office setting shall be 30 square feet (3 x 6).
- Due to the need to efficiently use limited space, managers and directors are not guaranteed an enclosed office. This determination will be made by the Asset Strategy team based on the available space and the role and responsibility of the manager or director.

Office here on level 4

Office walls currently shown aligning with exterior mullions. Alternatively could jog the walls to equalize the office sizes

4 offices to be same size

President (not CEO) is the only large office

Move Intensivist office down into ICU (was about 50 feet north)

Need to maintain dead-end corridor less than 20 feet

Extend multi-purpose room and have glass as corridor end

Specialty room count/location same for all floors

Individual of Size Isolation

Isolation

Swap with Nurse Manager office so Lactation is on the edge of the unit

Aisle with POCT counter ideally would be 6'

Aisle ideally would be 4'

RT Shared with 134 sf

RT Dirty 178 sf

RT Clean 166 sf

Check if aisle widths can be more narrow. Mike suggests using 5' 6" here since POCT is shifting away

Dictation door to nurse station not side corridor


1 controlled public entry

Individual of Size Isolation

Isolation

LEGEND - DEPARTMENT FUNCTION

- ACUTE CARE
- ACUTE CARE - SUPPORT
- ACUTE CARE - CIRCULATION
- ADMINISTRATION - SUPPORT
- ADMINISTRATION - CIRCULATION
- CRITICAL CARE
- CRITICAL CARE - SUPPORT
- CRITICAL CARE - CIRCULATION
- MINOR
- OP & D&T
- PUBLIC
- PUBLIC - CIRCULATION
- PUBLIC ELEVATOR
- SHELL
- SPECIALTY
- STAIRS
- STAFFMATE ELEVATOR

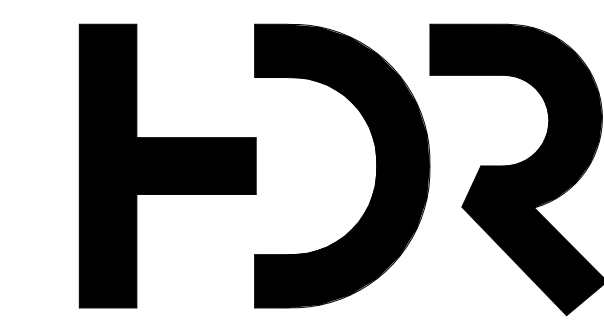

HDR ARCHITECTURE, INC.
4830 W KENNEDY BLVD #400
TAMPA, FL 33609
FL FIRM REG CERTIFICATION
AA-C000457

IBC 110.8.4.4 THRESHOLD BUILDING STATEMENT:
TO THE BEST OF THE ARCHITECT'S OR ENGINEER'S KNOWLEDGE, THE PLANS AND SPECIFICATIONS COMPLY WITH THE APPLICABLE MINIMUM BUILDING CODES AND THE APPLICABLE FIRE SAFETY STANDARDS AS DETERMINED BY THE LOCAL AUTHORITY IN ACCORDANCE WITH THIS SECTION AND CHAPTER 633, FLORIDA STATUTES.

ORLANDO HEALTH
166 INPATIENT BED
VIERA HOSPITAL

LAKE ANDREW DR & WILLET PLACE
MELBOURNE, FL 32940

ORLANDO HEALTH

PROJECT MANAGER	HDR ARCHITECTURE, INC.
PROJECT DESIGNER	HDR ARCHITECTURE, INC.
LANDSCAPE ARCHITECT	LANDSCAPE ARCHITECT
CIVIL ENGINEER	BSE CONSULTANTS, an LIA COMPANY
STRUCTURAL ENGINEER	WALTER P MOORE & ASSOCIATES, INC.
MECHANICAL ENGINEER	BR-A CONSULTING ENGINEERS, INC.
ELECTRICAL ENGINEER	BR-A CONSULTING ENGINEERS, INC.
PLUMBING ENGINEER	BR-A CONSULTING ENGINEERS, INC.
INTERIOR DESIGNER	HDR ARCHITECTURE, INC.
EQUIPMENT PLANNER	COVALUS
WAYFINDING	HDR ARCHITECTURE, INC.

SHEET REVIEWER Author

MARK DATE DESCRIPTION

AHCA NUMBER 23/23960034-(TBD)
PROJECT NUMBER 10427132
ORIGINAL ISSUE 09/26/2025

PRELIMINARY
NOT FOR CONSTRUCTION


Sheet Name

DEPARTMENT FUNCTION
ROOM FLOOR PLAN -
LEVEL 03

Sheet Number

G-403

Project Status
SCHEMATIC DESIGN

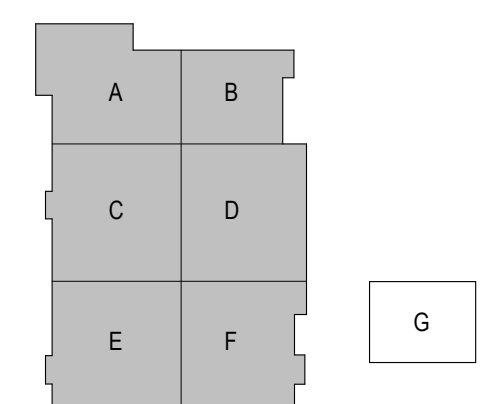

DEPARTMENT FUNCTION ROOM FLOOR PLAN - LEVEL 03

1" = 20'-0"